PROPOSED RESIDENTIAL BUILDING OWNED BY SIMI JOSEPH K.

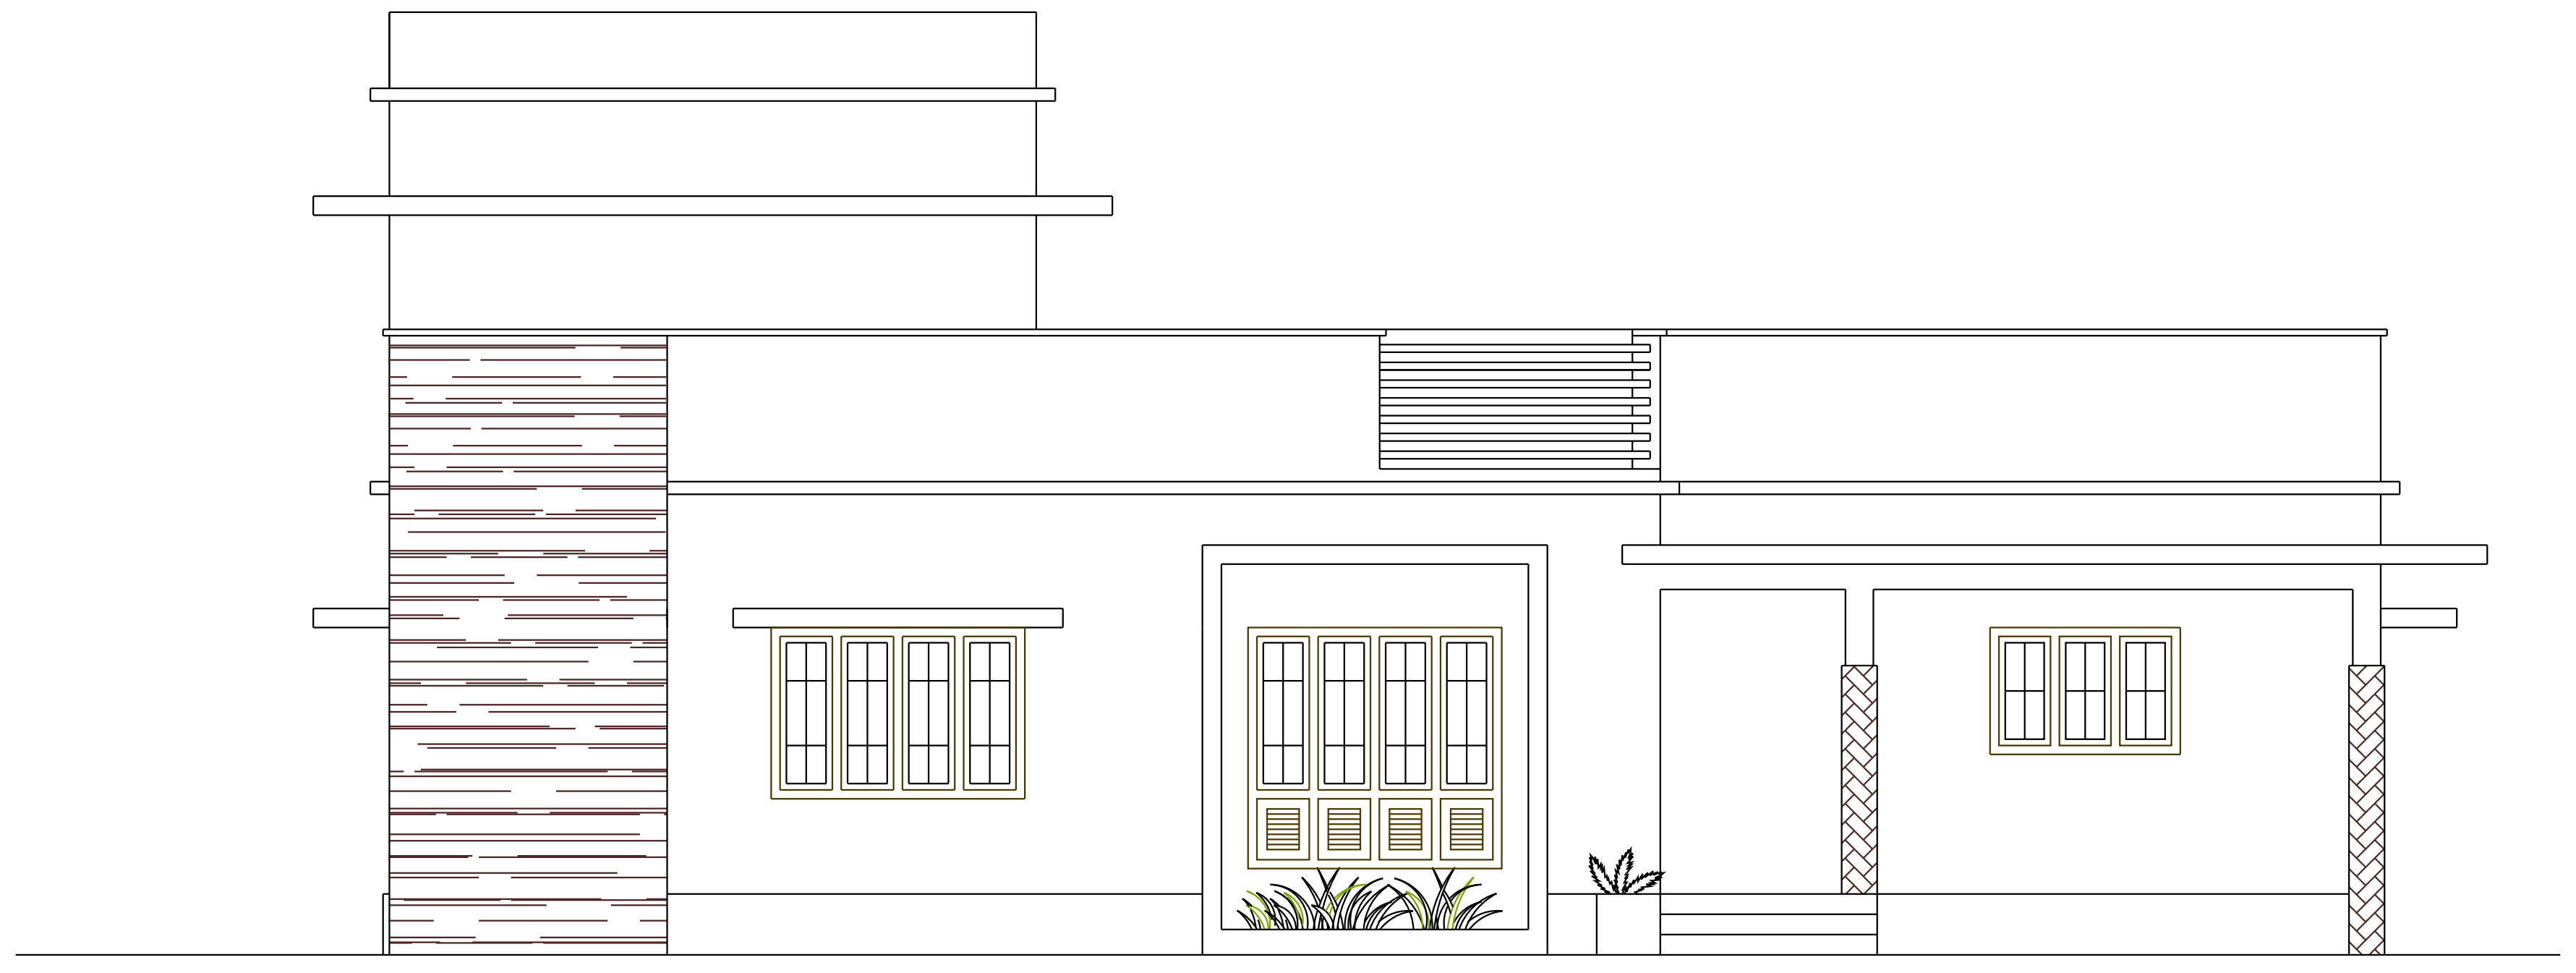

ELEVATION

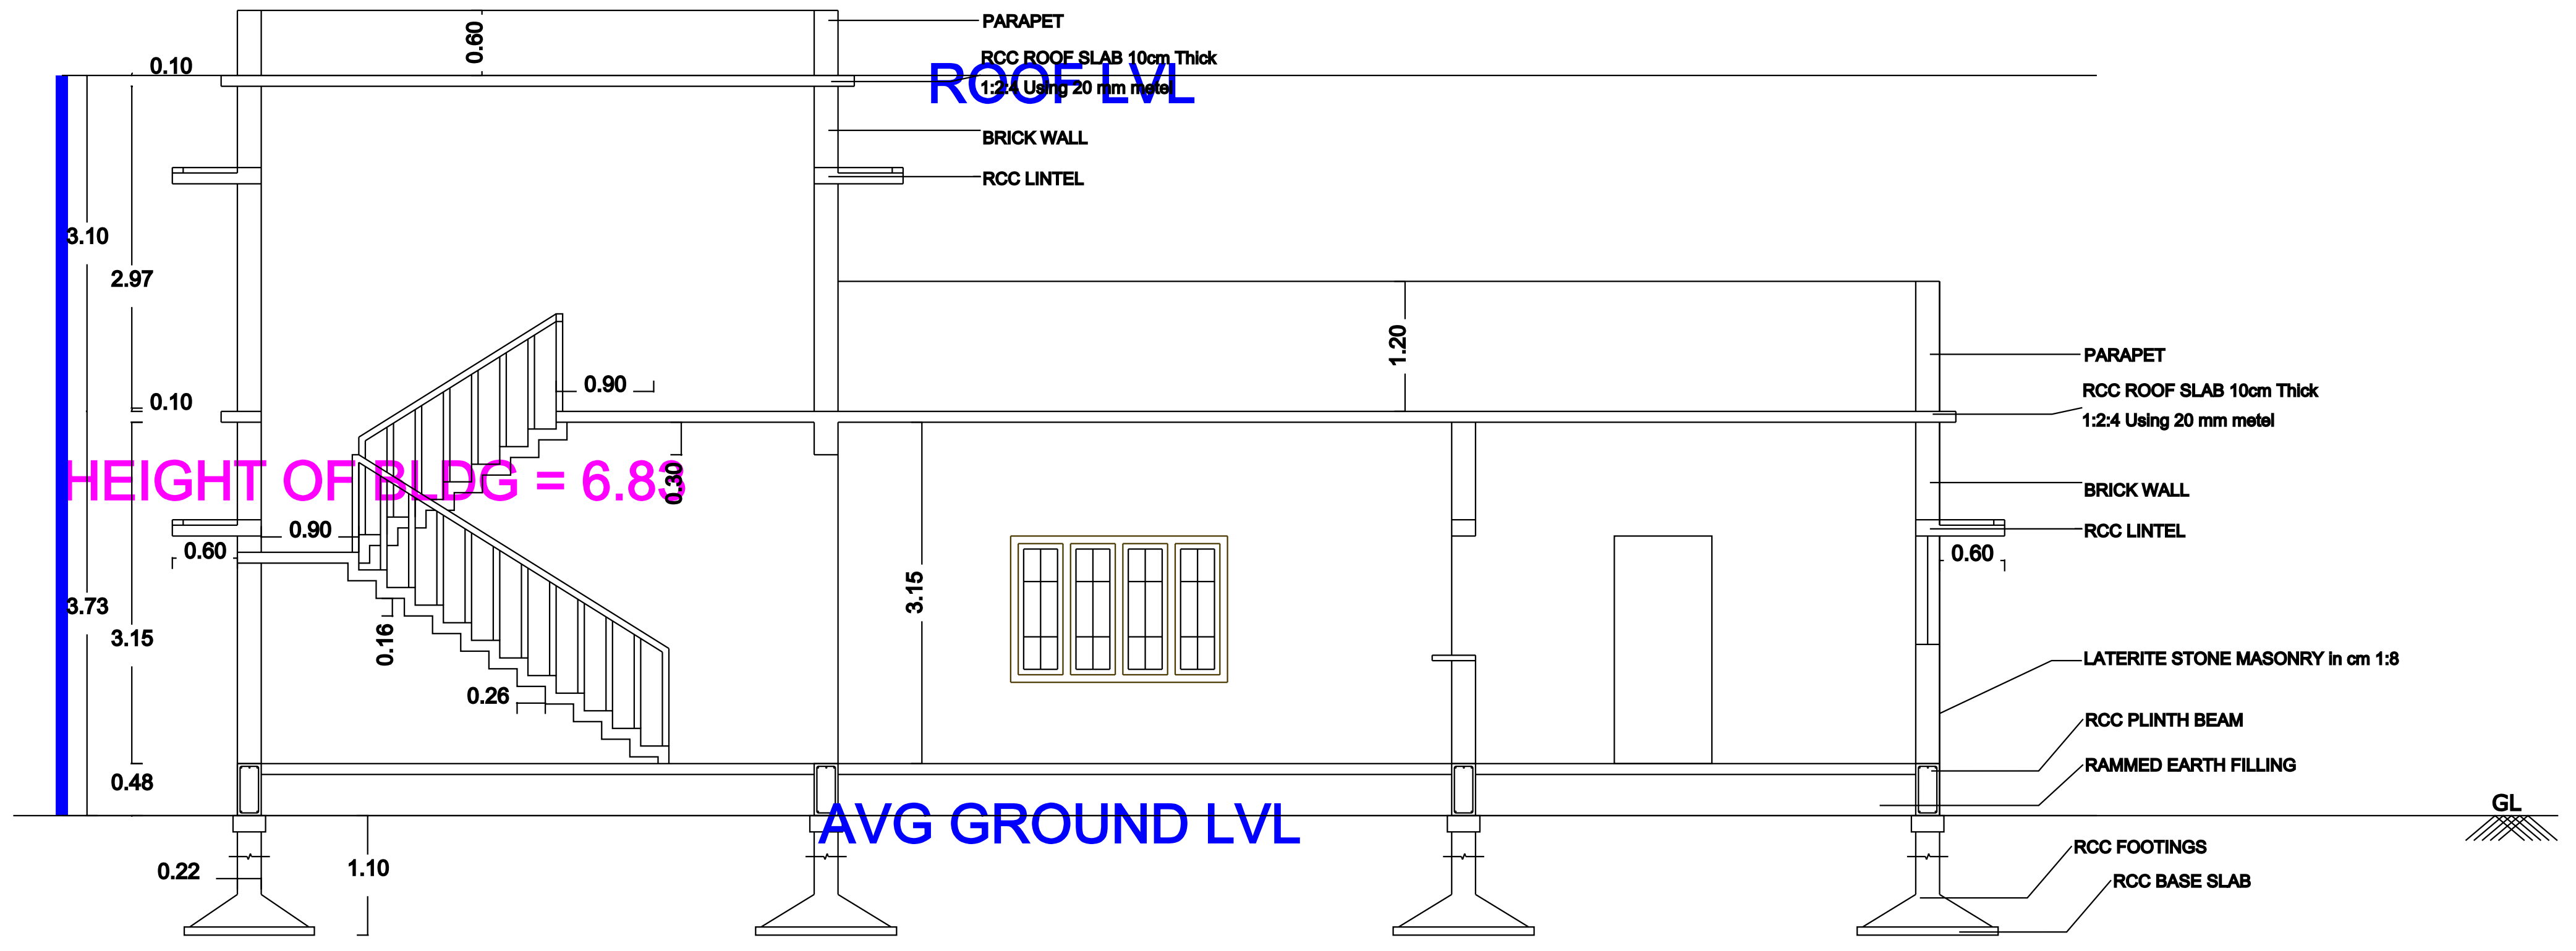

SECTION ON A-A

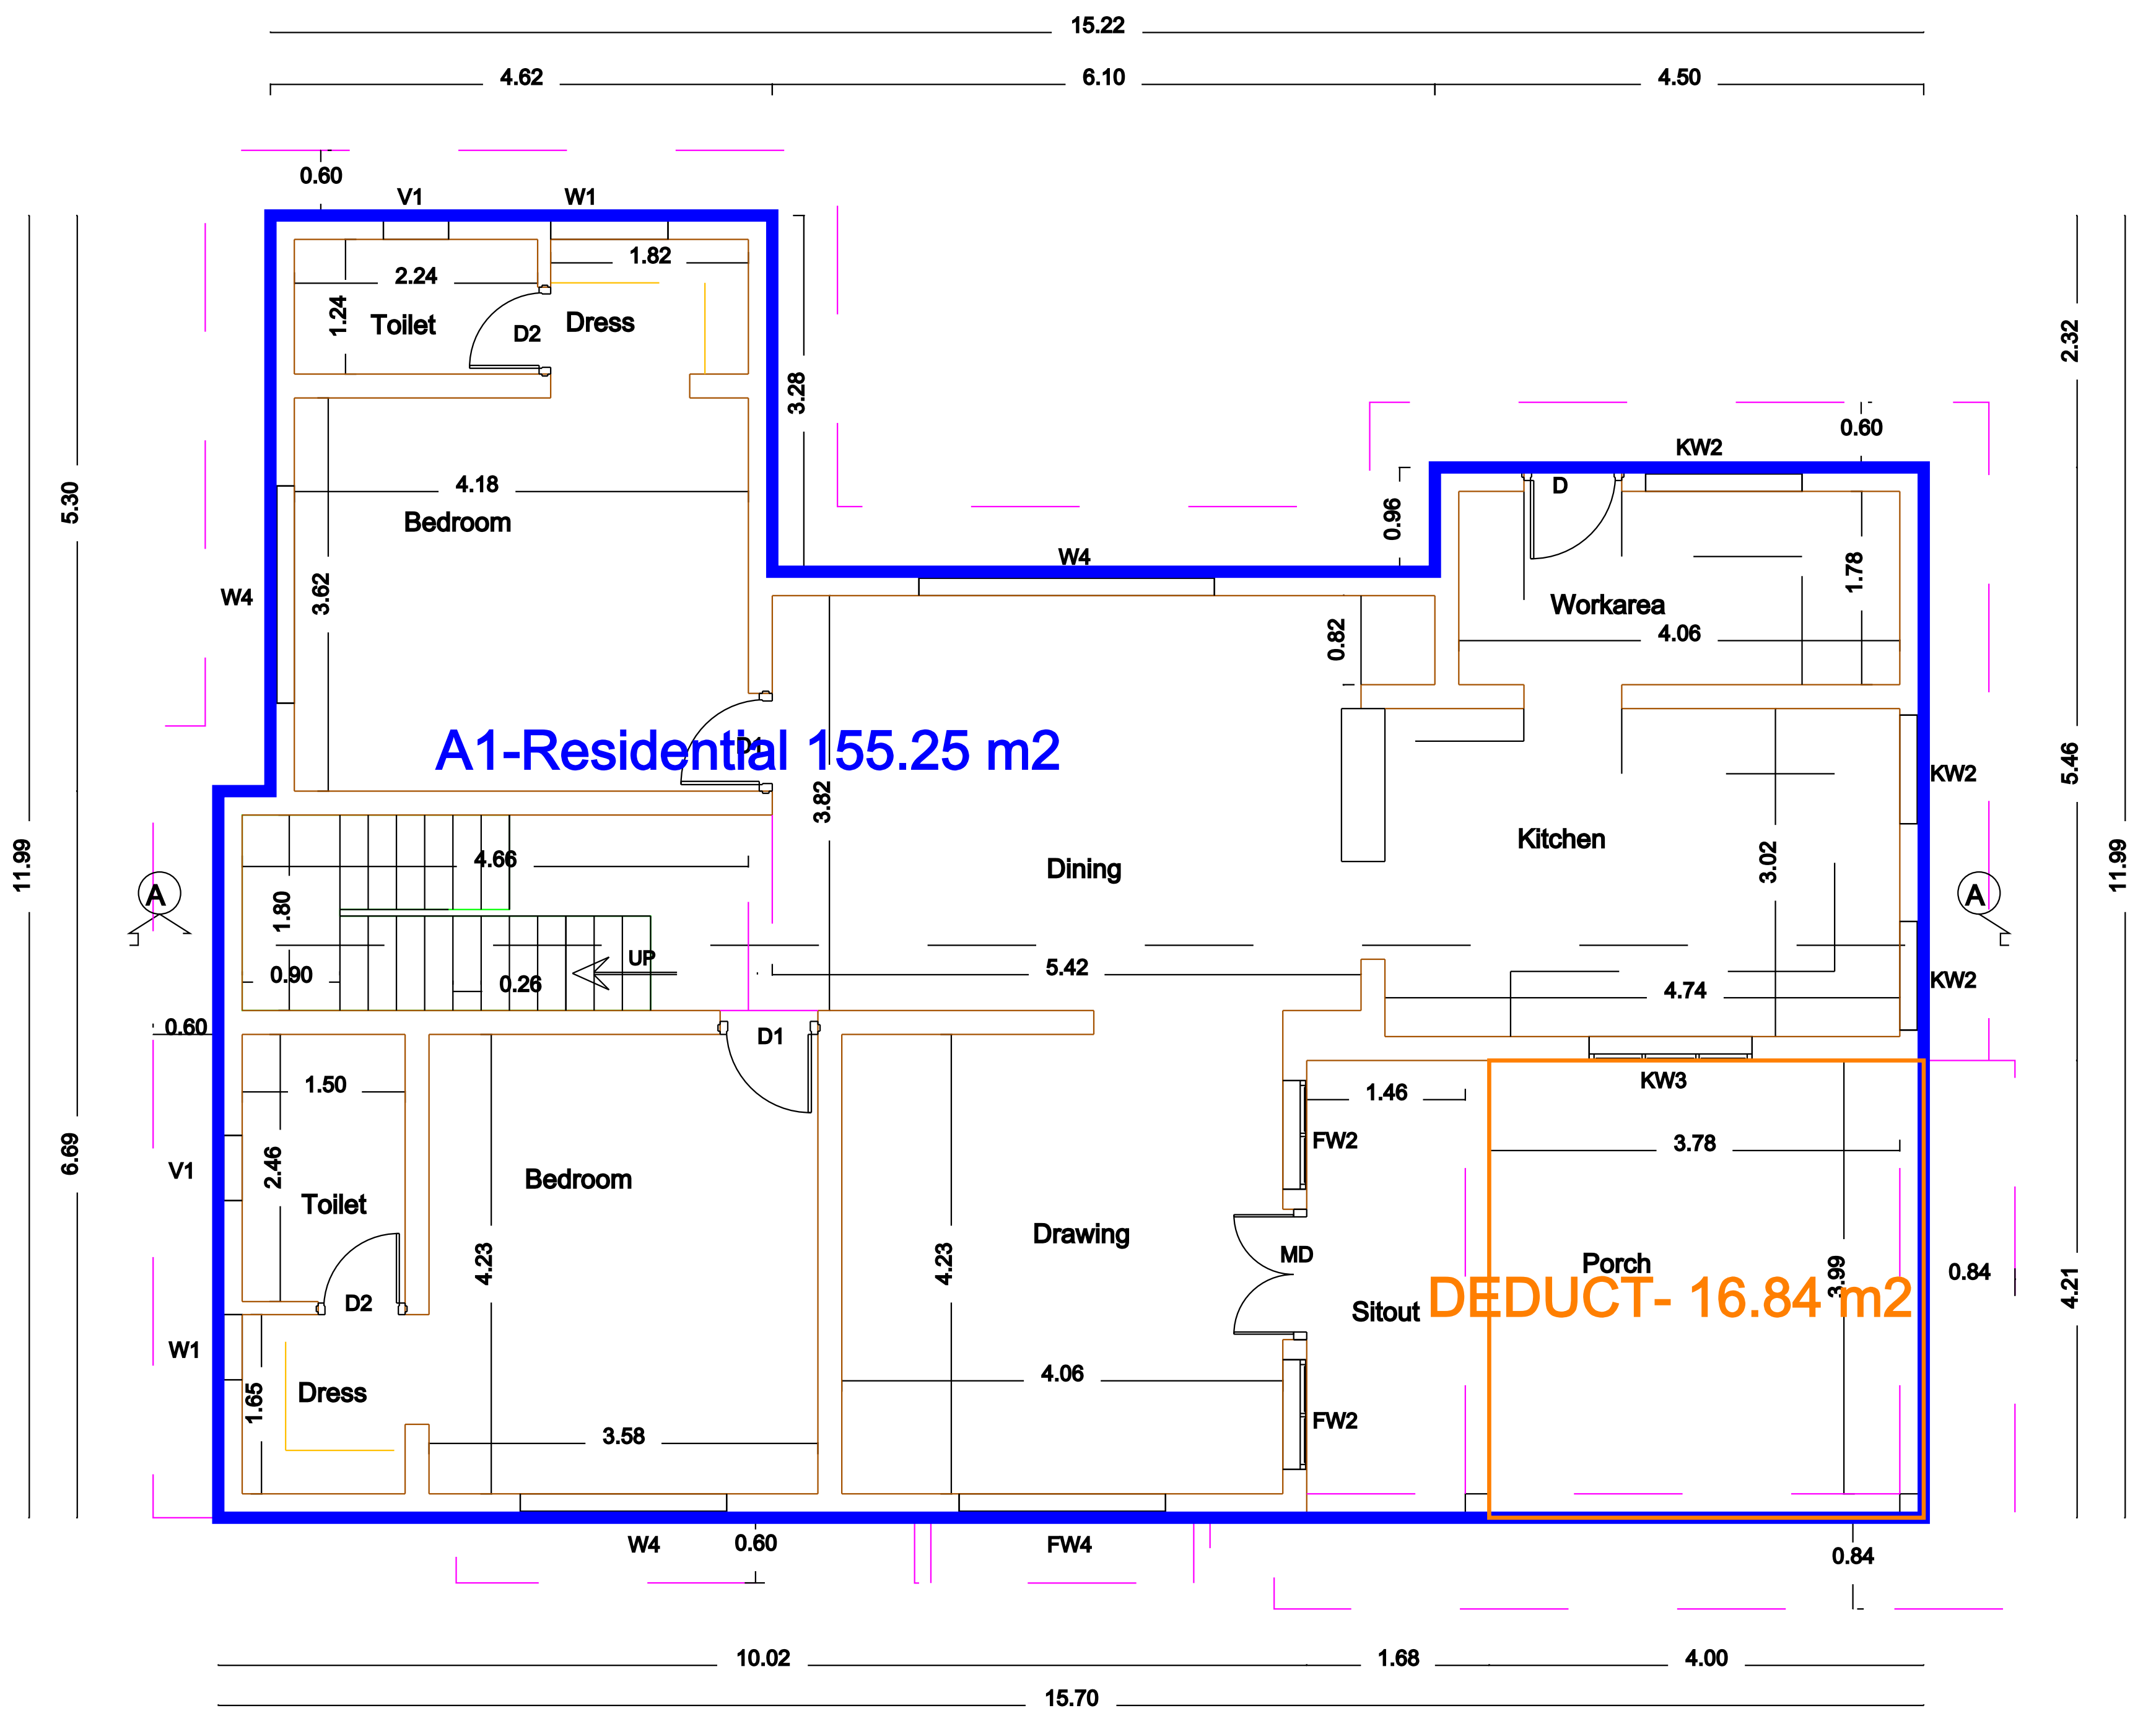

GROUND FLOOR PLAN

SOUTH

FACED RESIDENCE

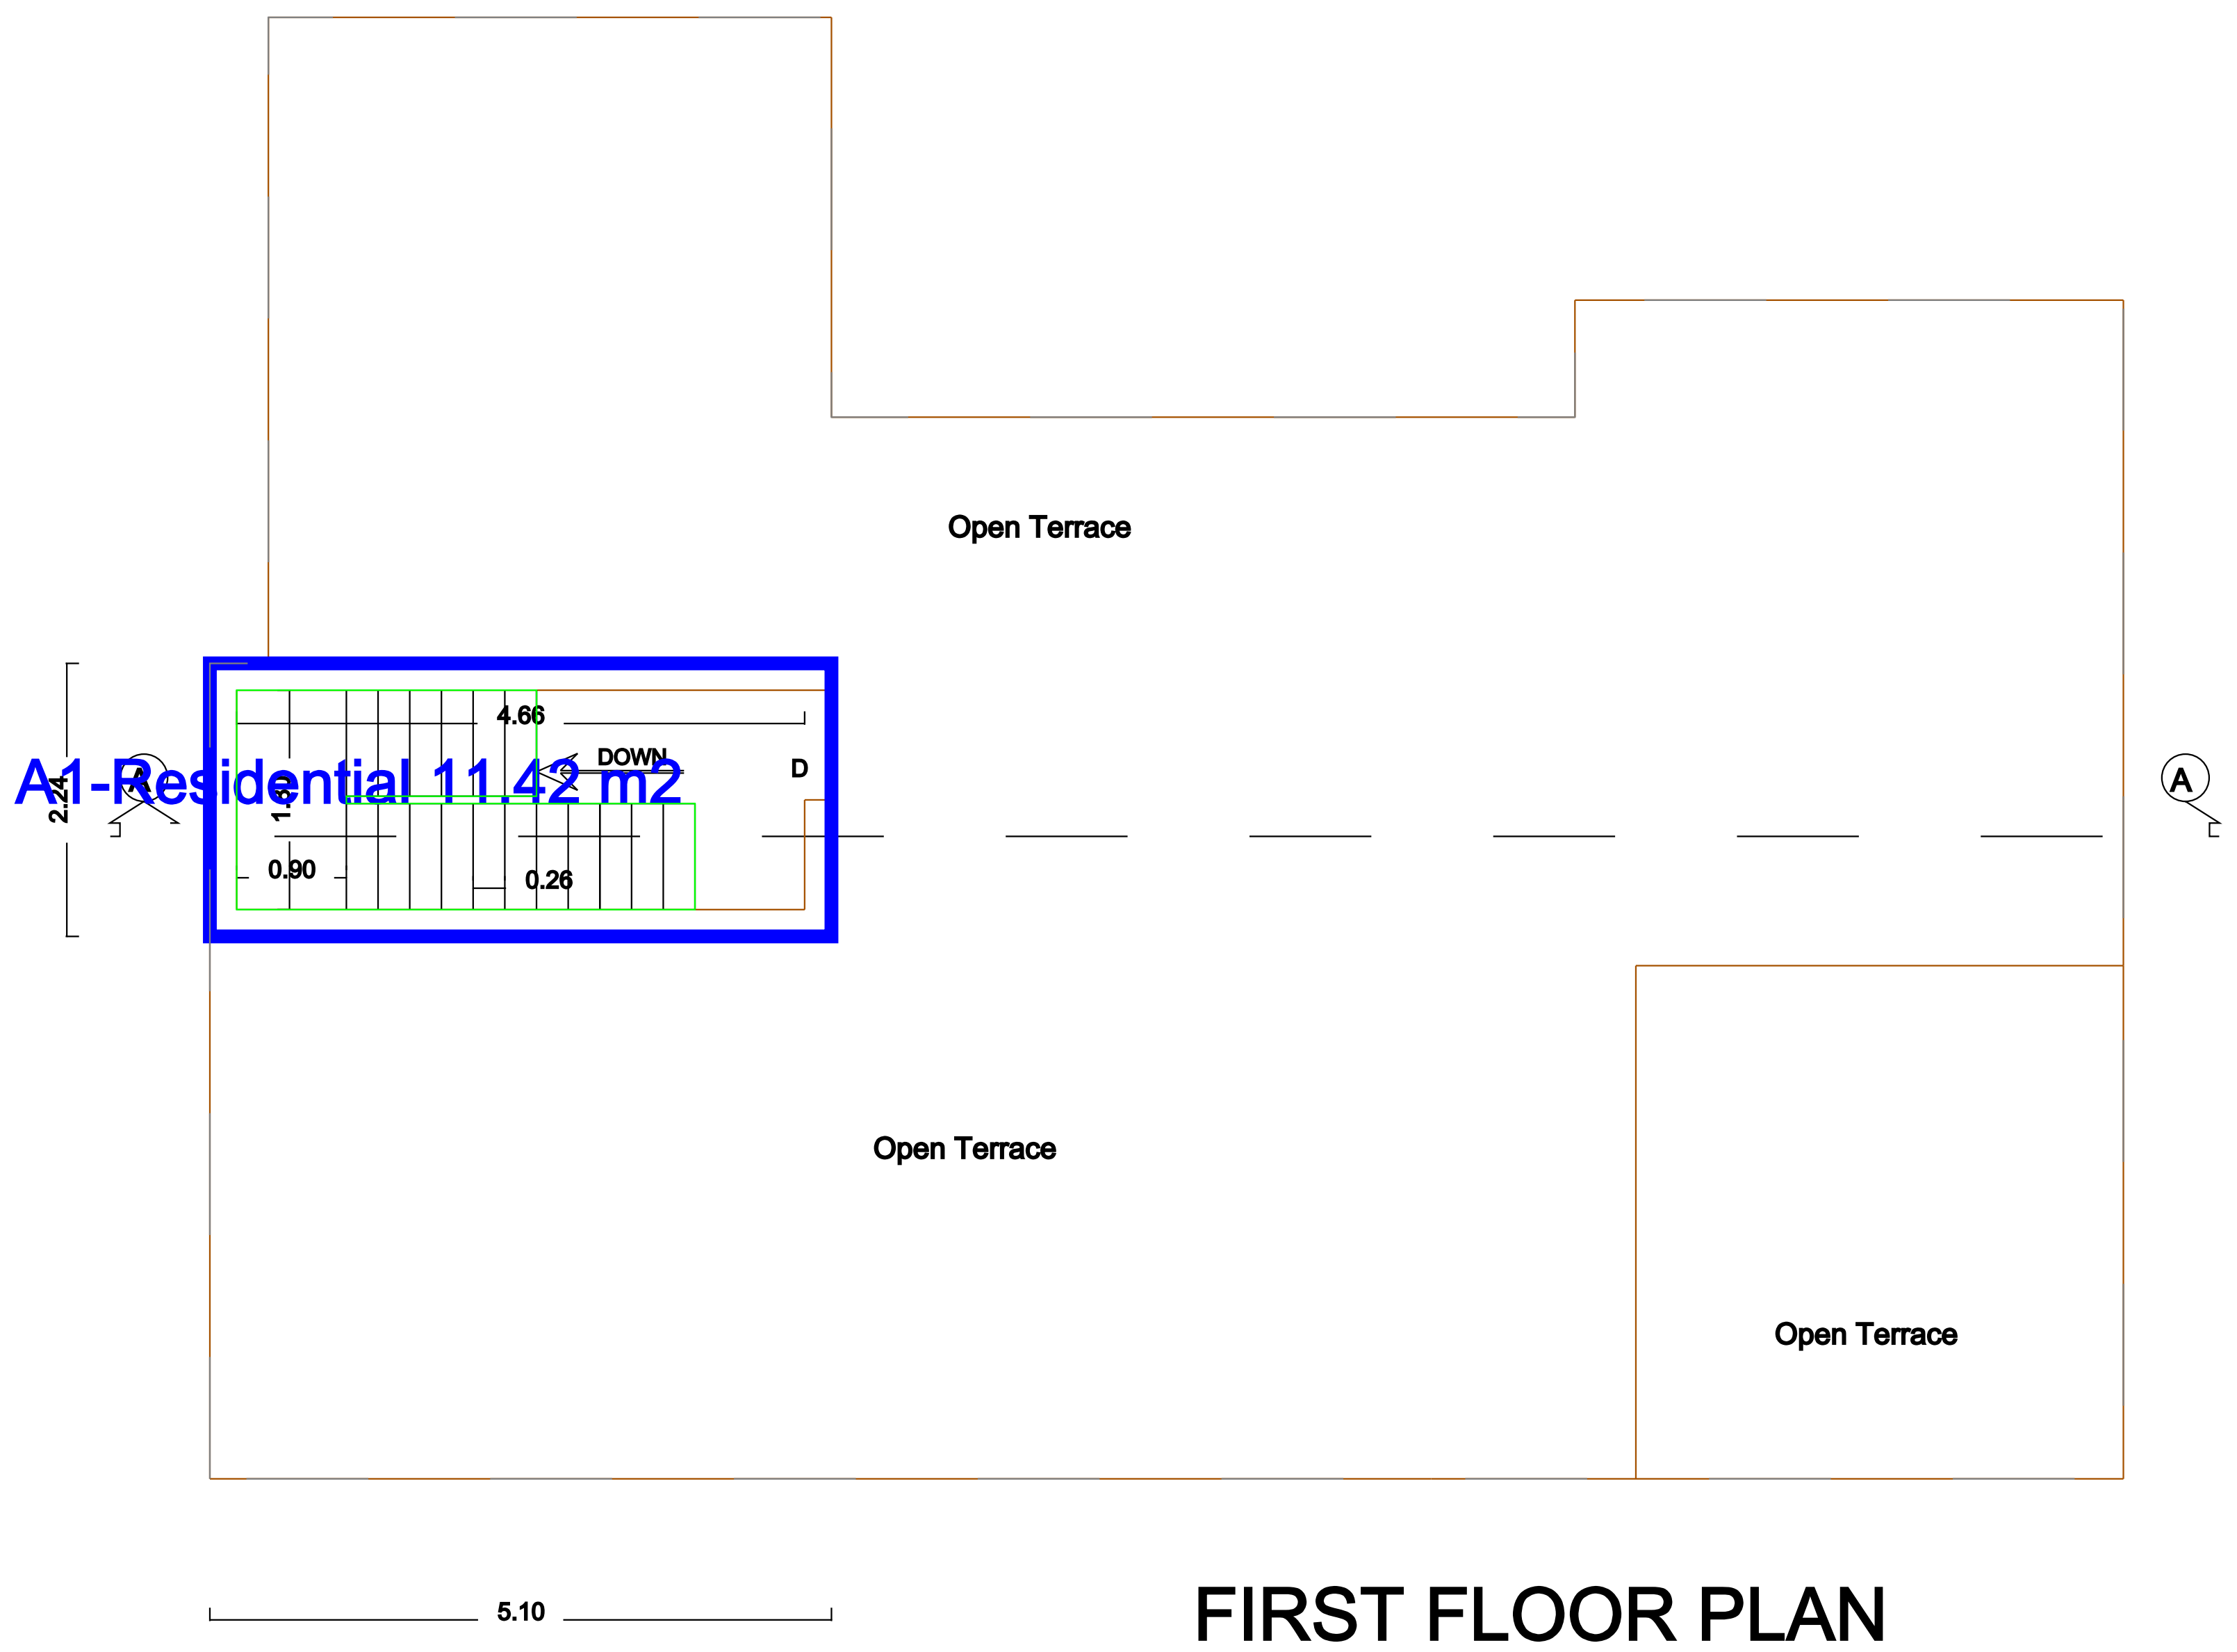

FIRST FLOOR PLAN

JOINERY DETAILS

SL.No.	ITEM		SIZE	No.
1.	DOOR(with bottam)	MD	120x210	1
2.	DOOR (with bottam)	D	90x210	2
3.	DOOR (without bottam)	D1	90x214	2
4.	DOOR (fiber/pvc)	D2	80x210	2
5.	WINDOW	FW4	200x180	1
6.	WINDOW	FW2	100x180	2
7.	WINDOW	W4	200x140	3
8.	WINDOW	W1	60x140	2
9.	WINDOW	KW3	150x100	1
10.	WINDOW	KW2	100x100	3
11.	VENTILATOR	V1	60x45	2

ALL DIMENSIONS ARE IN C.M's

Basement height - 45.00
Wall height - 315.00
Wall thickness - 22,18,12

STAIR -
Width - 90.00
Tread - 26.00
Riser - 16.00 (20 nos)
Landing - 90.00

PREPARED BY: PALAKUZHY ASSOCIATES
PUTHENCRUZ.P.O.,
Name :SINDHU .K.V Ph:- 9645224060
Email - palakuzhyassociates@gmail.com
Date:- 11-05-2026 Reg.No. :G6-4261/22/75/EB

TYPE OF OCCUPANCY :- RESIDENTIAL BUILDING

AREA STATEMENT [M2]

		BUILD UP AREA	FLOOR AREA
1.	FIRST FLOOR	11.42 Sq.Mt	11.42 Sq.Mt
2.	GROUND FLOOR	138.41 Sq.Mt	138.41 Sq.Mt
3.	PORCH	16.84 Sq.Mt	
	TOTAL	166.67 Sq.Mt	149.83 Sq.Mt

1.	F.S.I	149.83 / 718	0.21
2.	COVERAGE	155.25 / 718 x 100	21.62 %

APPLICATION FOR PERMIT OF A
RESIDENTIAL BUILDING FOR
SIMI JOSEPH K.
CATEGORY/OCCUPANCY: RESIDENCE
GROUP - A1

APPLICANT :-

SIMI JOSEPH K.
PATTASSERIL (H)
PUTHENCRUZ P. O.,
CHERUKUNNU KARA
ERNAKULAM, Pin:- 682303
Ph:- 9633175006

LAND PARTICULARS

1.	PANCHAYATH	AIKARANAD
2.	VILLAGE	AIKARANAD NORTH
3.	TALUK	KUNNATHUNAD
4.	DISTRICT	ERNAKULAM
5.	WARD No.	16
6.	Old- SURVEY No.	221/15-2, 2215-3
7.	EXTENT	(359+359)= 718 Sq.Mt
8.	Re- SURVEY BLOCK	44
9.	THANDAPPER No.	6768
10.	NEAREST Bldg No.	16 / 423
11.	KSEB Post No.	P / VB / 36

OWNER DETAILS

Address:

Pattasseril,Puthencruz,Puthencruz (PO),Ernakulam,682308

Owners:

1 : Simi Joseph K, e-Verified On: 13-05-2026, 01:11:21 PM

+ Total 1 owner(s), All e-Verified, (Ref. Appendix A1 for details)

APPENDIX- J1
[See rule 6(3)]
CERTIFICATE

Certified that:

(i) the plot boundaries, measurements and other details shown in the site plan are correct and
(ii) the drawings are in conformity with the provisions of the Master Plan/Detailed Town Planning Scheme/Interim Development Order as applicable under the Kerala Town and Country Planning Act 2016.
(iii) the drawings are in conformity with the provisions of the Kerala Panchayath Building Rules, 2019 and other applicable statutes.

E-verified: 13-05-2026 13:02:49
Name: SINDHU K V

License Category	Registration Number
SENIOR-SUPERVISOR-REGULAR-LICENSE	G4/3803/18/82/SS_03/12/2018_02/12/2022
ENGINEER-B-EMPANELLED-LICENSE	EMP:F4-6873/2023/39/EB/LSGD/JD/EKM_27/11/2023_26/11/2027
ENGINEER-B-REGULAR-LICENSE	G6-4261/22/75/EB_13/12/2022_12/12/2026
SUPERVISOR-A-REGULAR-LICENSE	G6/3377/11/341/SA_26/12/2011_25/12/2014
SUPERVISOR-B-REGULAR-LICENSE	L2-9171/07/8158/SB_29/10/2007_28/10/2010

APPENDIX- J2
[See rule 9(2)]
CERTIFICATE

Certified that:

(i) the document(s) in support of the ownership of the plot has/have been verified and that the applicant(s) has/have every right of construction in this plot.
(ii) the plot boundaries, measurements and other details shown in the site plan have been verified at site and found correct and
(iii) the drawings are in conformity with the provisions of the Master Plan/Detailed Town Planning Scheme/Interim Development Order as applicable under the Kerala Town and Country Planning Act 2016.
(iv) the drawings are in conformity with the provisions of the Kerala Panchayath Building Rules, 2019 and other applicable statutes.

Name: Mohammad hashim p a,Designation: Grama Panchayats Secretary
Aikaranad Grama Panchayat

AIKARANAD GRAMA PANCHAYAT
BUILDING PERMIT DOCUMENT

PERMIT NO: SCP/21453/2026-Revision-01, FILE NO: 3537603-2026
VALIDITY OF PERMIT: 23-02-2026 TO 22-02-2031
APPROVED BY: Mohammad hashim p a(Grama Panchayats Secretary)
REVIEWED BY: Shameer p a(Head Clerk)
FIELD VERIFIED BY: Ashadevi b(Assistant Engineer)

This is a computer generated authentication and doesn't require Signature or Seal in original

Signature Not Verified
Digitally signed by P A MOHAMMAD HASHIM
Date: 2026.06.02 12:45:09 IST
Reason: Building permit